


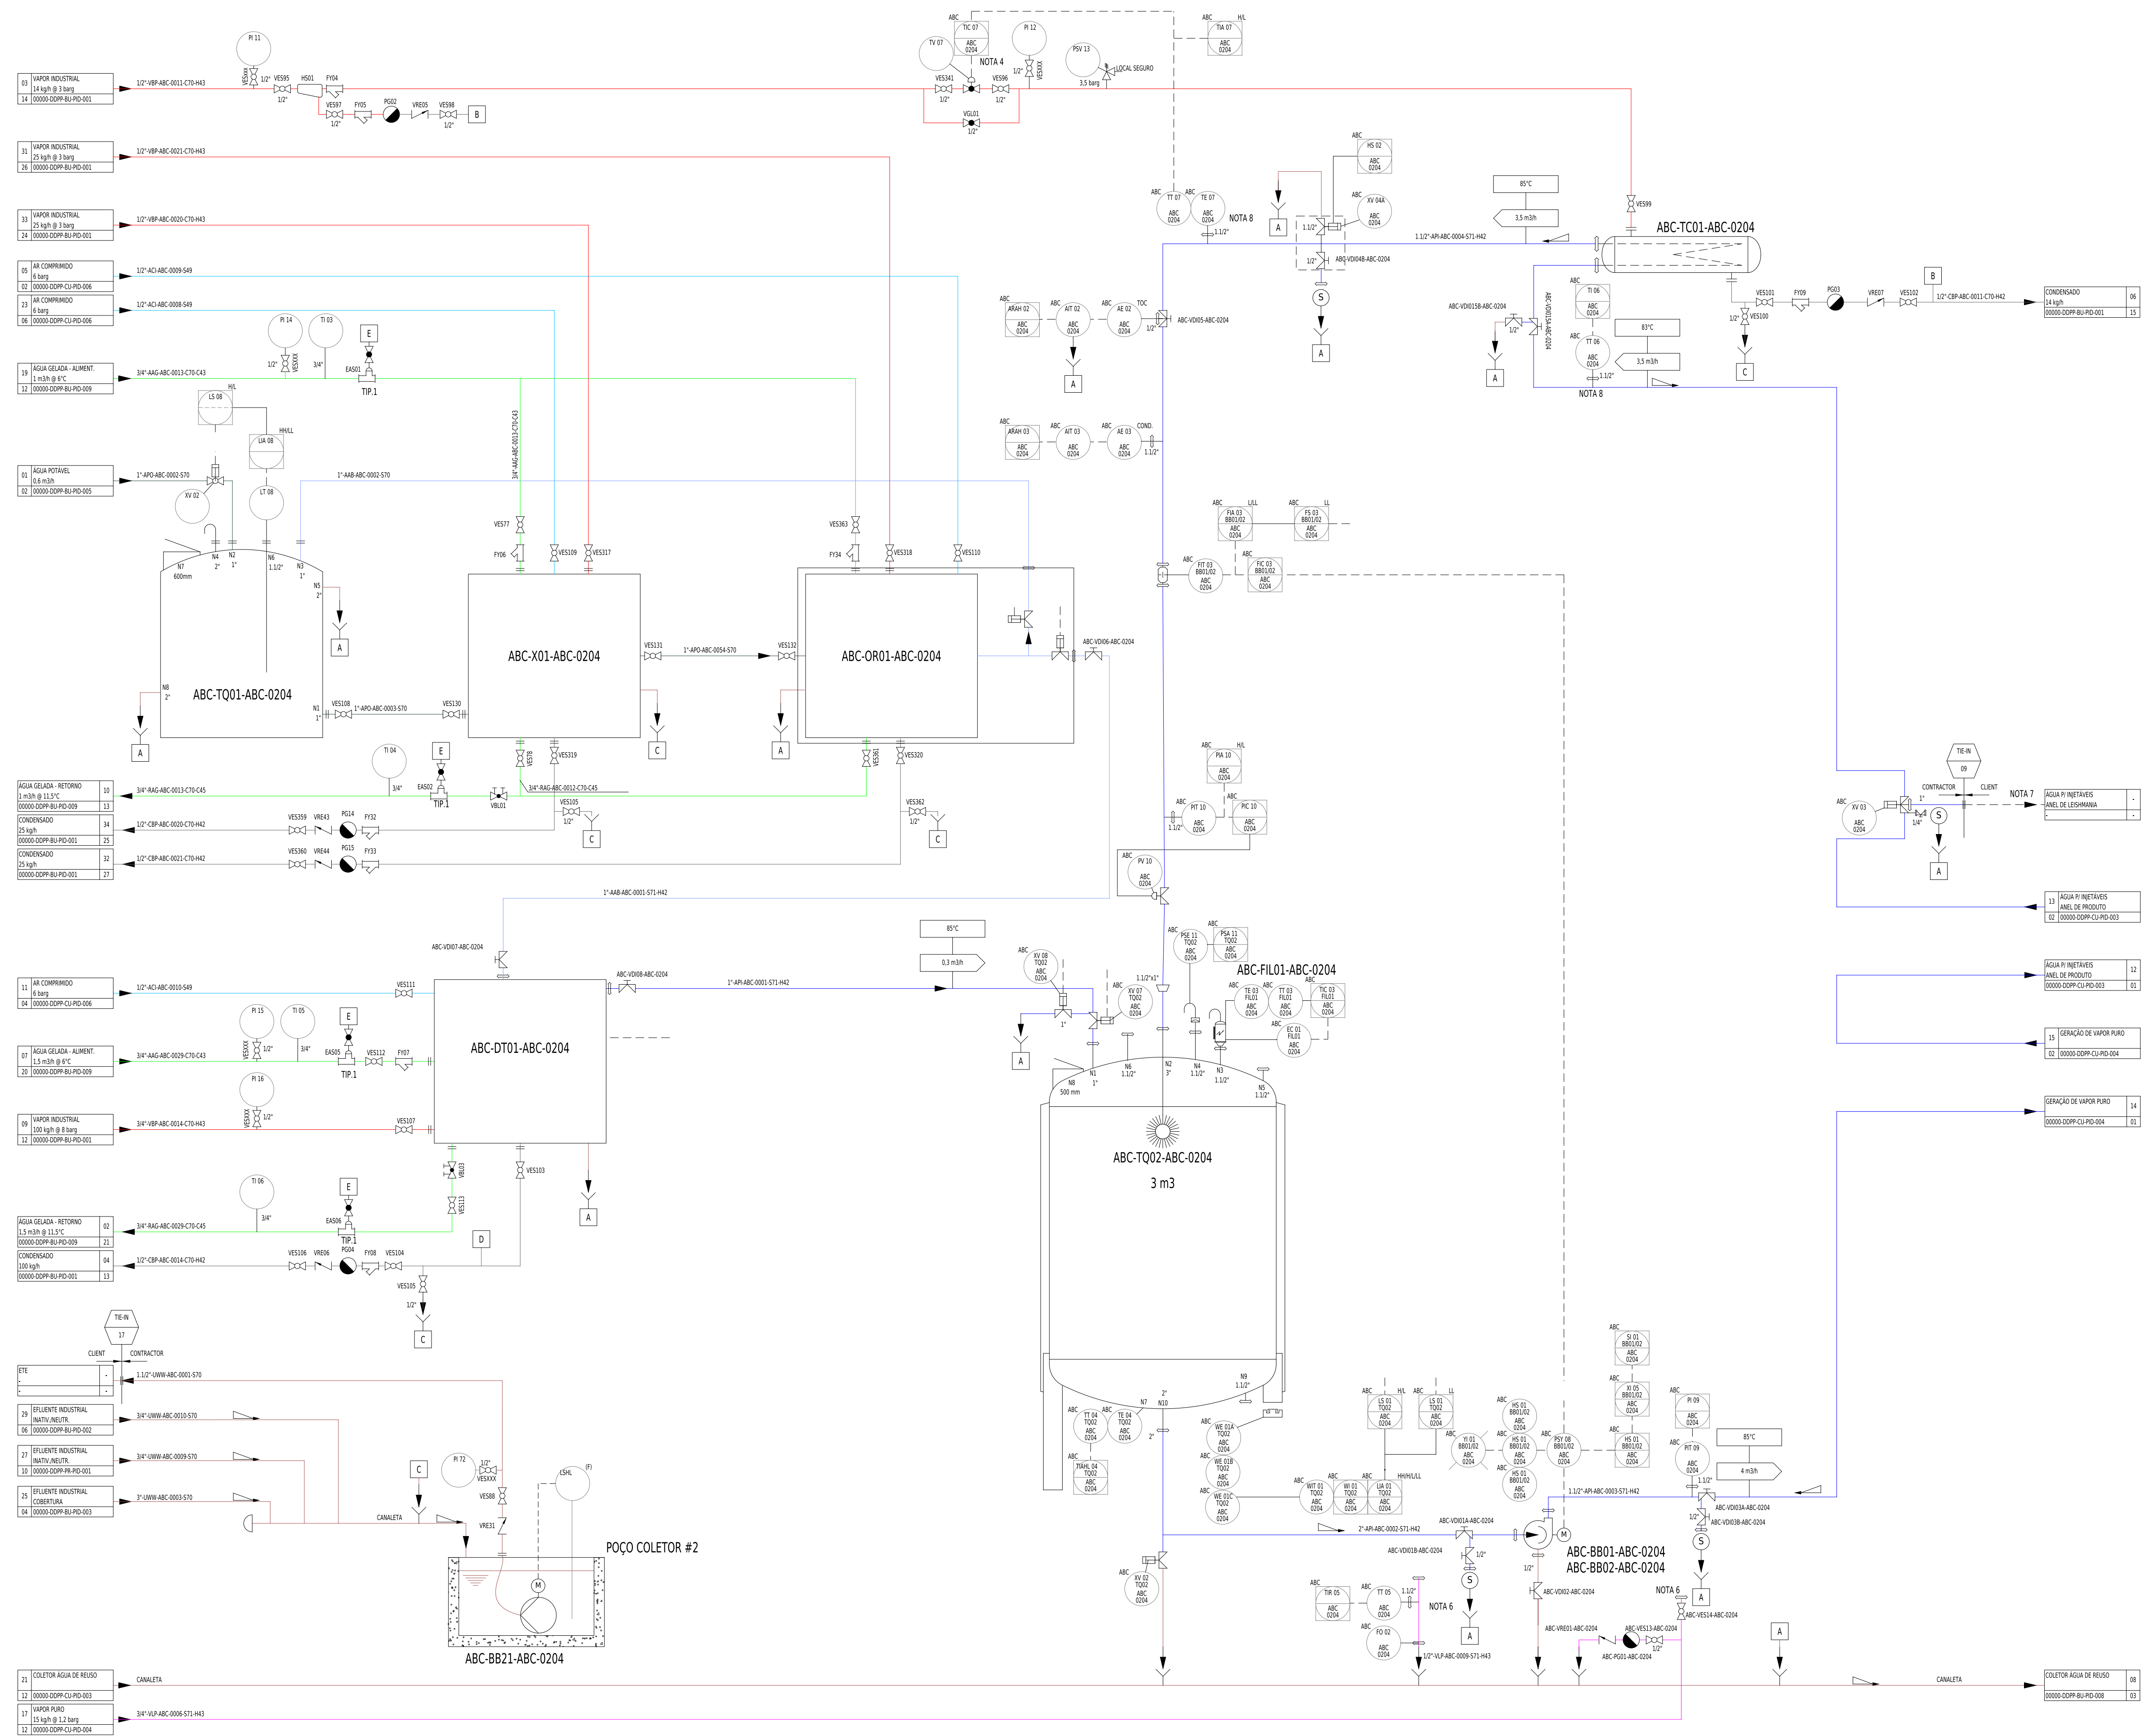

ABC-TQ01-ABC-0204	ABC-X01-ABC-0204	ABC-OR01-ABC-0204	ABC-DT01-ABC-0204	ABC-TQ02-ABC-0204	ABC-BB01/02-ABC-0204	ABC-FIL01-ABC-0204	ABC-TC01-ABC-0204	ABC-BB21-ABC-0204
NOME: TANQUE DE ÁGUA POTÁVEL	NOME: PRÉ-TRATAMENTO	NOME: OSMOSE REVERSA	NOME: DESTILADOR	NOME: TANQUE DE API	NOME: BOMBA DE API	NOME: FILTRO VENT	NOME: TROCADOR DE CALOR	NOME: BOMBA
TIPO: -	TIPO: FILTRAÇÃO	TIPO: SIMPLES PASSO	TIPO: MULTIEFEITO	TIPO: TORISFÉRICO	TIPO: CENTRÍFUGA	TIPO: HIDROFÓBICO ESTÉRIL	TIPO: CASCO E TUBOS	TIPO: SUBMERSÍVEL
CAPACIDADE: 5 m3	CAPACIDADE: 450 Lh	CAPACIDADE: 450 L/h	CAPACIDADE: 300 L/h	CAPACIDADE: 3 m3	CAPACIDADE: 4 m3/h	CAPACIDADE: 4 m3/h	CAPACIDADE: 8.2 kW	CAPACIDADE: 4.0 m3/h